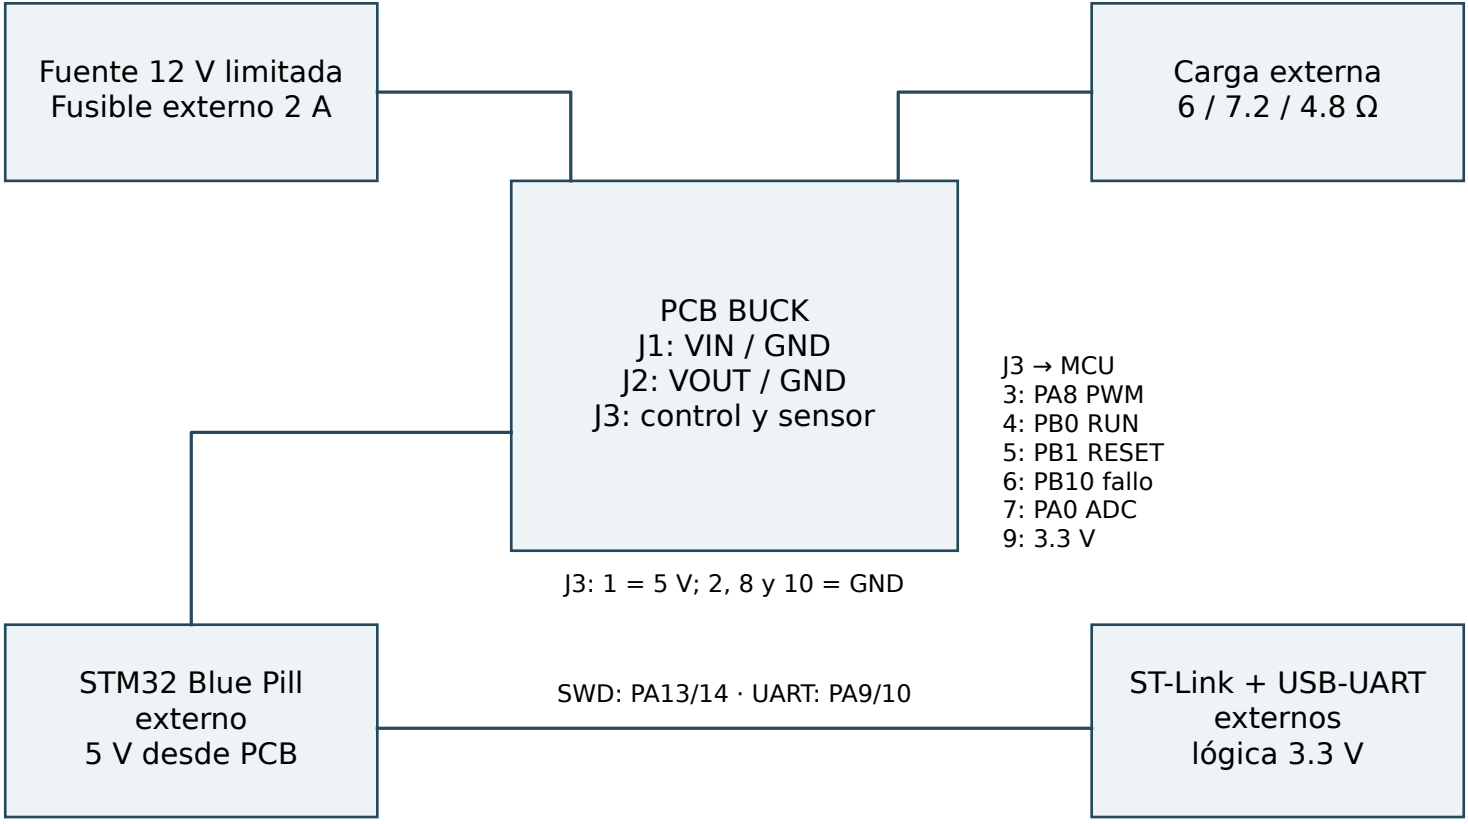CONEXIONES PREVISTAS · MONTAJE PENDIENTE